
1

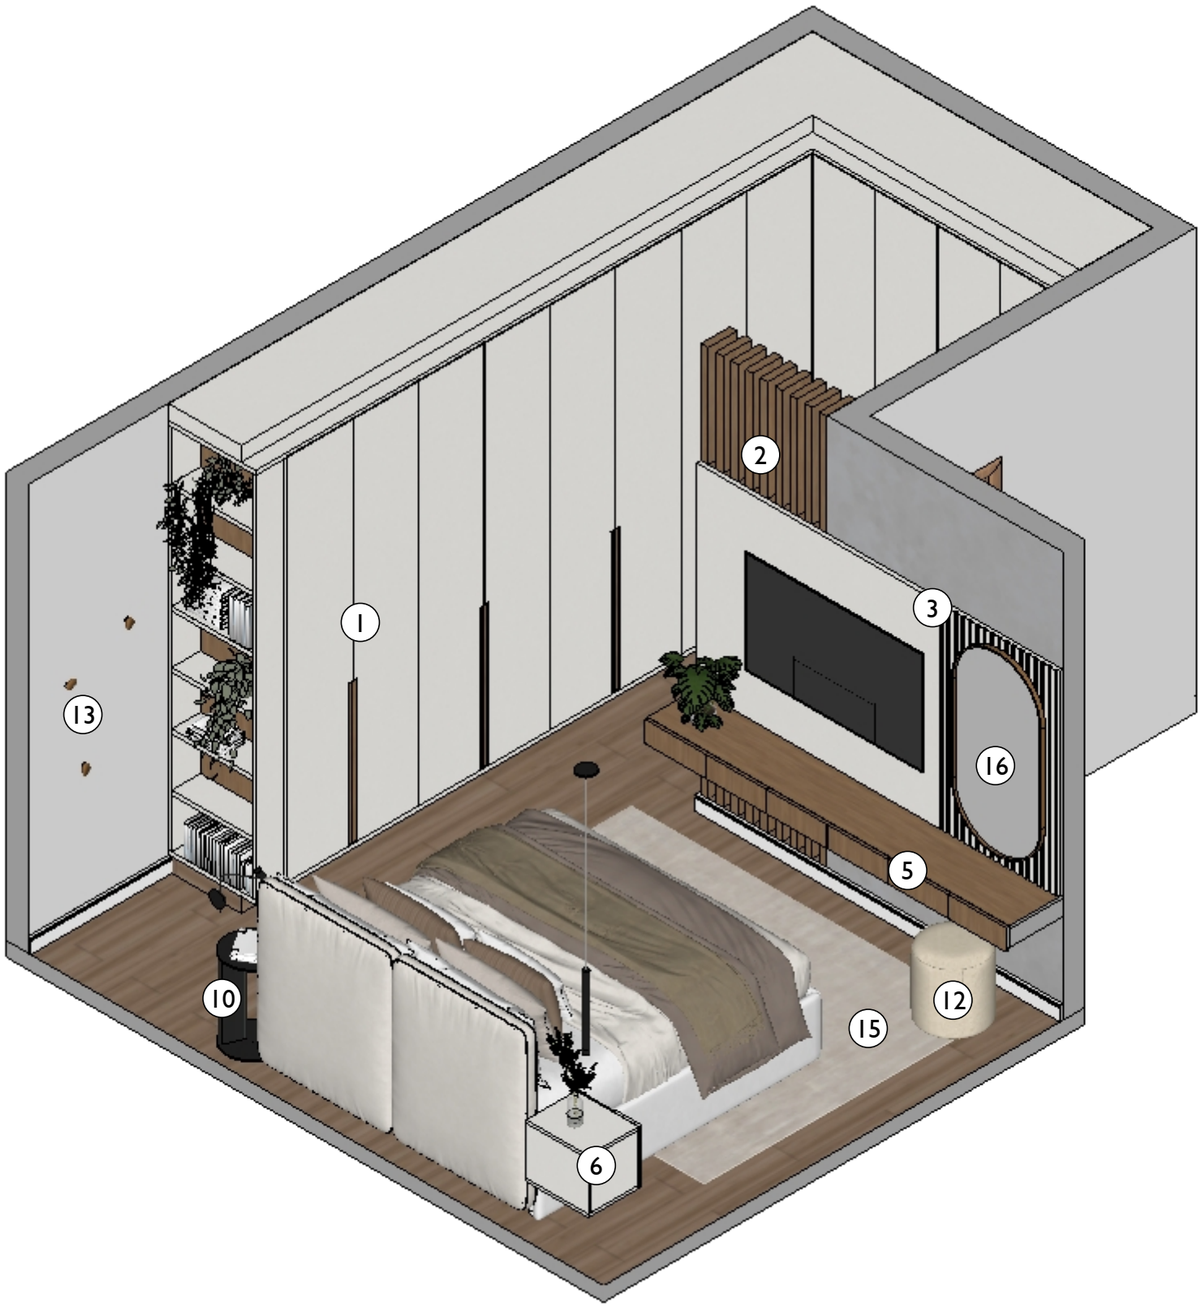

VISTA ISOMÉTRICA
escala: 1/30


ATENÇÃO: CONFERIR TODAS AS MEDIDAS NO LOCAL

LEGENDA		
SIMB.	DESCRIÇÃO	QTD.
	MARCENARIA	
1	Guarda Roupas em MDF Arauco	01
2	Divisória em MDF Arauco Amendoeira com nichos em MDF Arauco Lino	01
3	Painel TV em MDF Arauco Lino	01
4	Cabeceira em MDF Arauco Amendoeira	01
5	Aparador em MDF Arauco Amendoeira	01
6	Mesa de Cabeceira em MDF Arauco Lino	01
	VIDRAÇARIA	
7	Espelho 60x200cm	01
	ILUMINAÇÃO	
8	Arandela de Parede Metal Preto - Portofino	01
9	Pendente LED Dunn Cilíndrico 3000K 3W Metal Preto - Nordecor	01
	MÓVEIS SOLTOS	
10	Mesa Lateral Apoio Chanfrada na cor Preta - Westwing	01
11	Quadro Decorativo Norwich Quadrada Art Tonial	01
12	Puff Orgânico Living Mavi Bouclê Bege - Desk Design Bege	02
13	Trio de penduradores Petra	01
14	Tapete Astúrias Champagne -150cm	01
15	Tapete Loop Creme - 200x250cm	01
16	Espelho oval Oruy Elisse com moldura em Couro Caramelo - 50x110cm	01
	REVESTIMENTO PAREDE	
1	Parede emassada e pintada na cor Branco Neve acab. Fosco fabricante Suvinil	
2	Parede emassada e pintada em Cimento Queimado Platina - Maza	

QUARTO SUÍTE CAMILA E OTÁVIO
estúdio vilel[a]rq
Rua Jarbas Pimenta, nº 254 - Centro - Boa Esperança (MG)

João Paulo Vilela | tel.: (35) 99277-5071

estúdio vilel[a]rq
ARQUITETURA & DESIGN

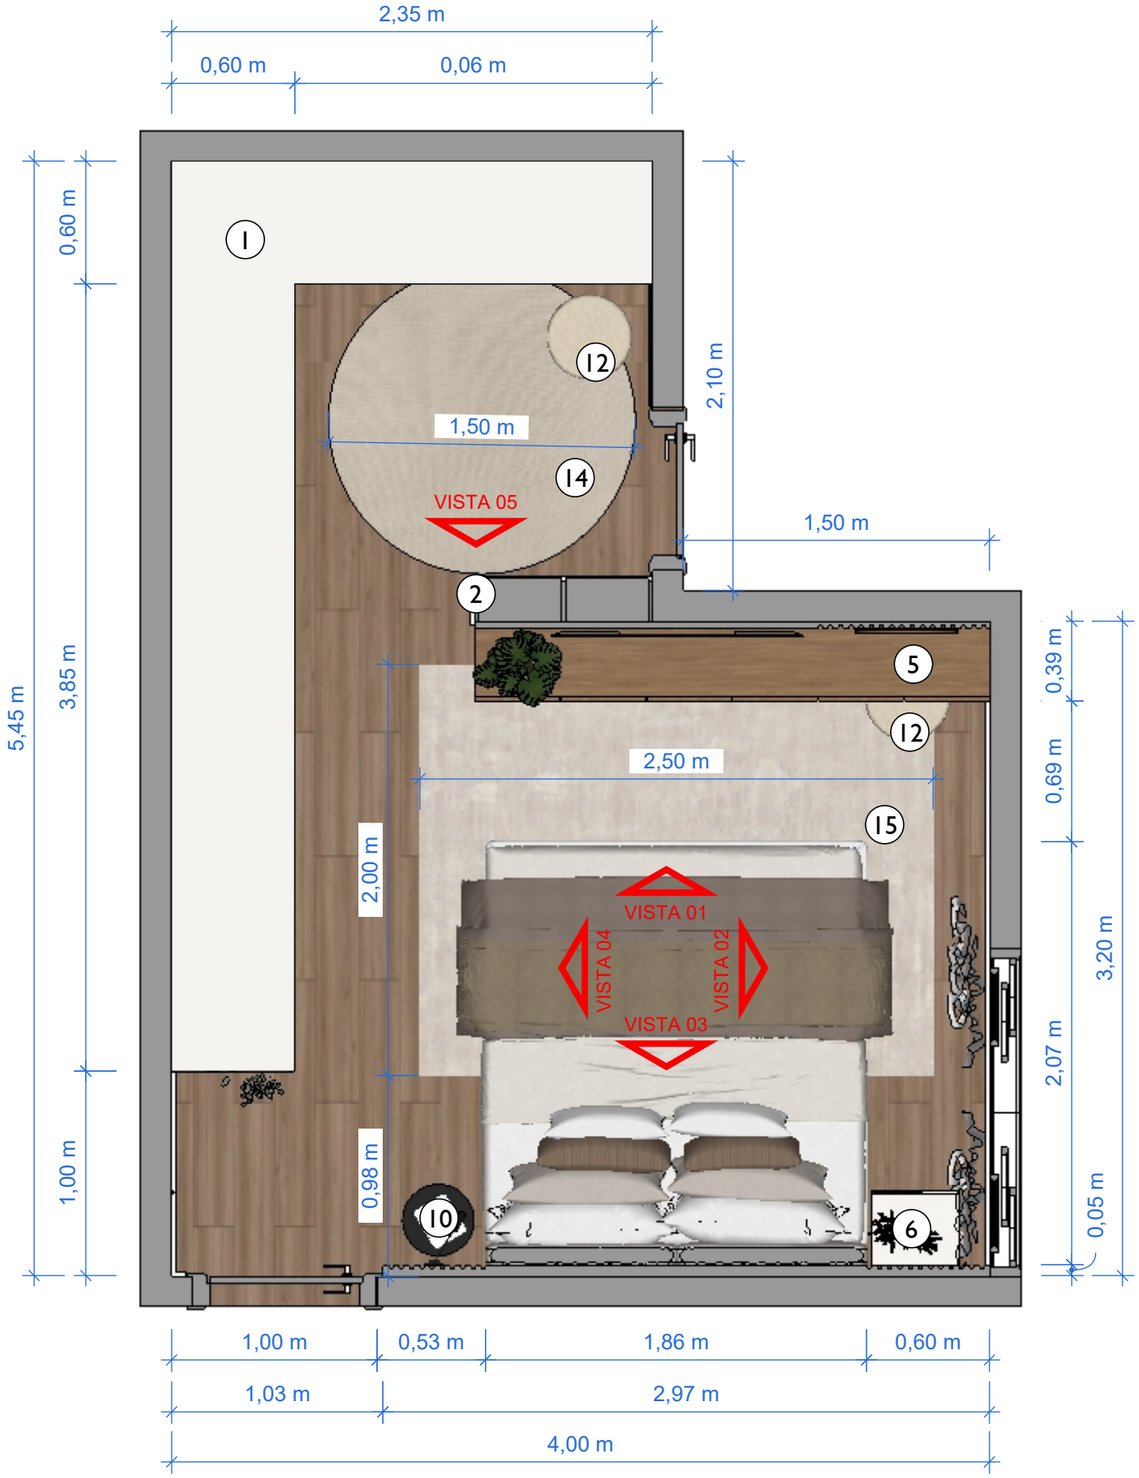

PLANTA BAIXA - HUMANIZADA
escala: 1/30

ATENÇÃO: CONFERIR TODAS AS MEDIDAS NO LOCAL


LEGENDA		
SIMB.	DESCRIÇÃO	QTD.
	MARCENARIA	
1	Guarda Roupas em MDF Arauco	01
2	Divisória em MDF Arauco Amendoeira com nichos em MDF Arauco Lino	01
3	Painel TV em MDF Arauco Lino	01
4	Cabeceira em MDF Arauco Amendoeira	01
5	Aparador em MDF Arauco Amendoeira	01
6	Mesa de Cabeceira em MDF Arauco Lino	01
	VIDRAÇARIA	
7	Espelho 60x200cm	01
	ILUMINAÇÃO	
8	Arandela de Parede Metal Preto - Portofino	01
9	Pendente LED Dunn Cilíndrico 3000K 3W Metal Preto - Nordecor	01
	MÓVEIS SOLTOS	
10	Mesa Lateral Apoio Chanfrada na cor Preta - Westwing	01
11	Quadro Decorativo Norwich Quadrada Art Tonial	01
12	Puff Orgânico Living Mavi Bouclê Bege - Desk Design Bege	02
13	Trio de penduradores Petra	01
14	Tapete Astúrias Champagne -150cm	01
15	Tapete Loop Creme - 200x250cm	01
16	Espelho oval Oruy Elisse com moldura em Couro Caramelo - 50x110cm	01
	REVESTIMENTO PAREDE	
1	Parede emassada e pintada na cor Branco Neve acab. Fosco fabricante Suvinil	
2	Parede emassada e pintada em Cimento Queimado Platina - Maza	

QUARTO SUÍTE CAMILA E OTÁVIO

estúdio vilel[a]rq
Rua Jarbas Pimenta, nº 254 - Centro - Boa Esperança (MG)
João Paulo Vilela | tel.: (35) 99277-5071

estúdio vilel[a]rq
ARQUITETURA & DESIGN

ATENÇÃO: CONFERIR TODAS AS MEDIDAS NO LOCAL

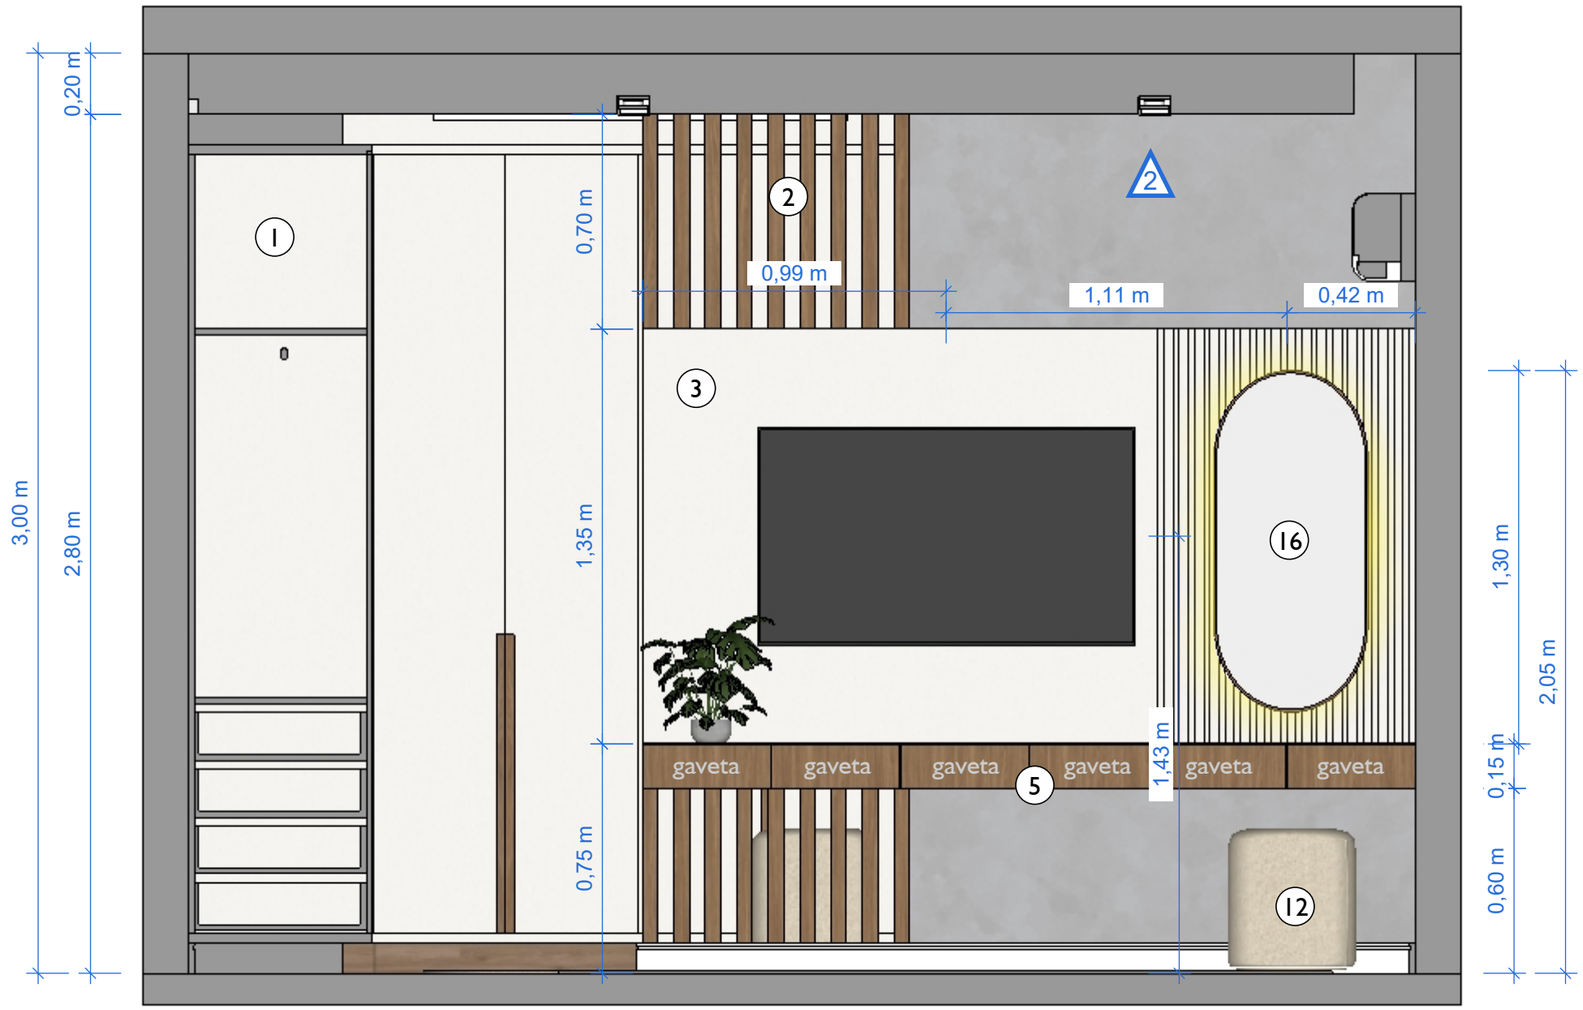

VISTA 01 - HUMANIZADA
escala: 1/20

QUARTO SUÍTE CAMILA E OTÁVIO
estúdio vilel[a]rq
Rua Jarbas Pimenta, nº 254 - Centro - Boa Esperança (MG)

João Paulo Vilela | tel.: (35) 99277-5071

estúdio vilel[a]rq
ARQUITETURA & DESIGN

ATENÇÃO: CONFERIR TODAS AS MEDIDAS NO LOCAL




VISTA 02 - HUMANIZADA
escala: 1/20

QUARTO SUÍTE CAMILA E OTÁVIO
estúdio vilel[a]rq
Rua Jarbas Pimenta, nº 254 - Centro - Boa Esperança (MG)

João Paulo Vilela | tel.: (35) 99277-5071

estúdio vilel[a]rq
ARQUITETURA & DESIGN

ATENÇÃO: CONFERIR TODAS AS MEDIDAS NO LOCAL

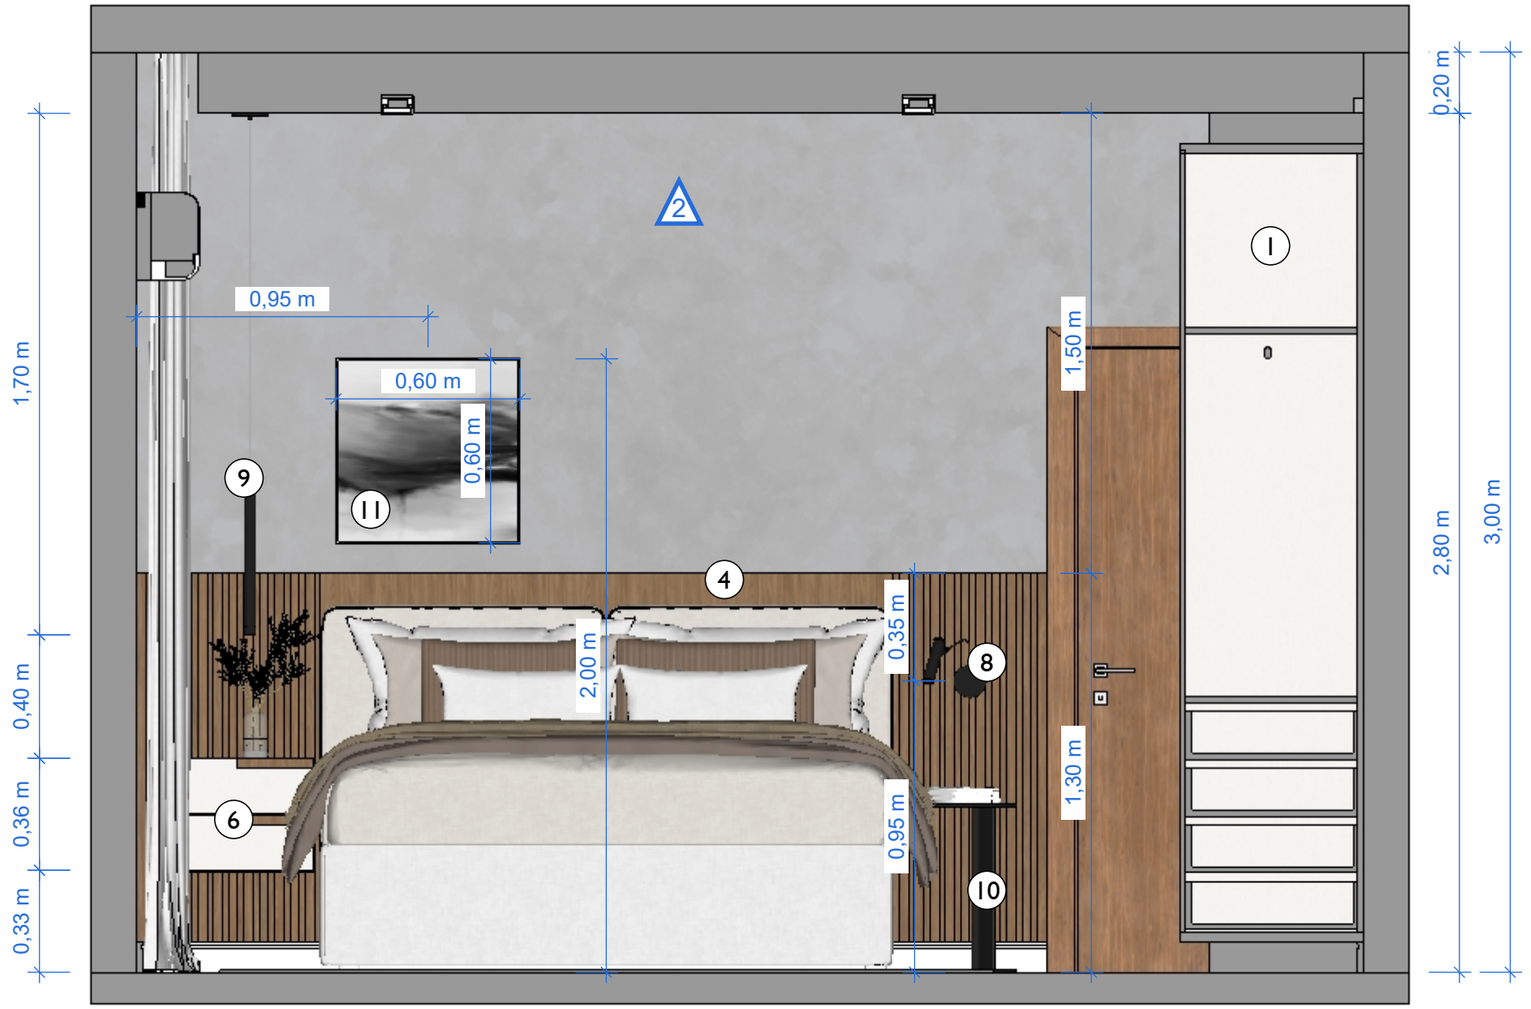


VISTA 03 - HUMANIZADA
escala: 1/20

QUARTO SUÍTE CAMILA E OTÁVIO
estúdio vilel[a]rq
Rua Jarbas Pimenta, nº 254 - Centro - Boa Esperança (MG)

João Paulo Vilela | tel.: (35) 99277-5071

estúdio vilel[a]rq
ARQUITETURA & DESIGN

ATENÇÃO: CONFERIR TODAS AS MEDIDAS NO LOCAL

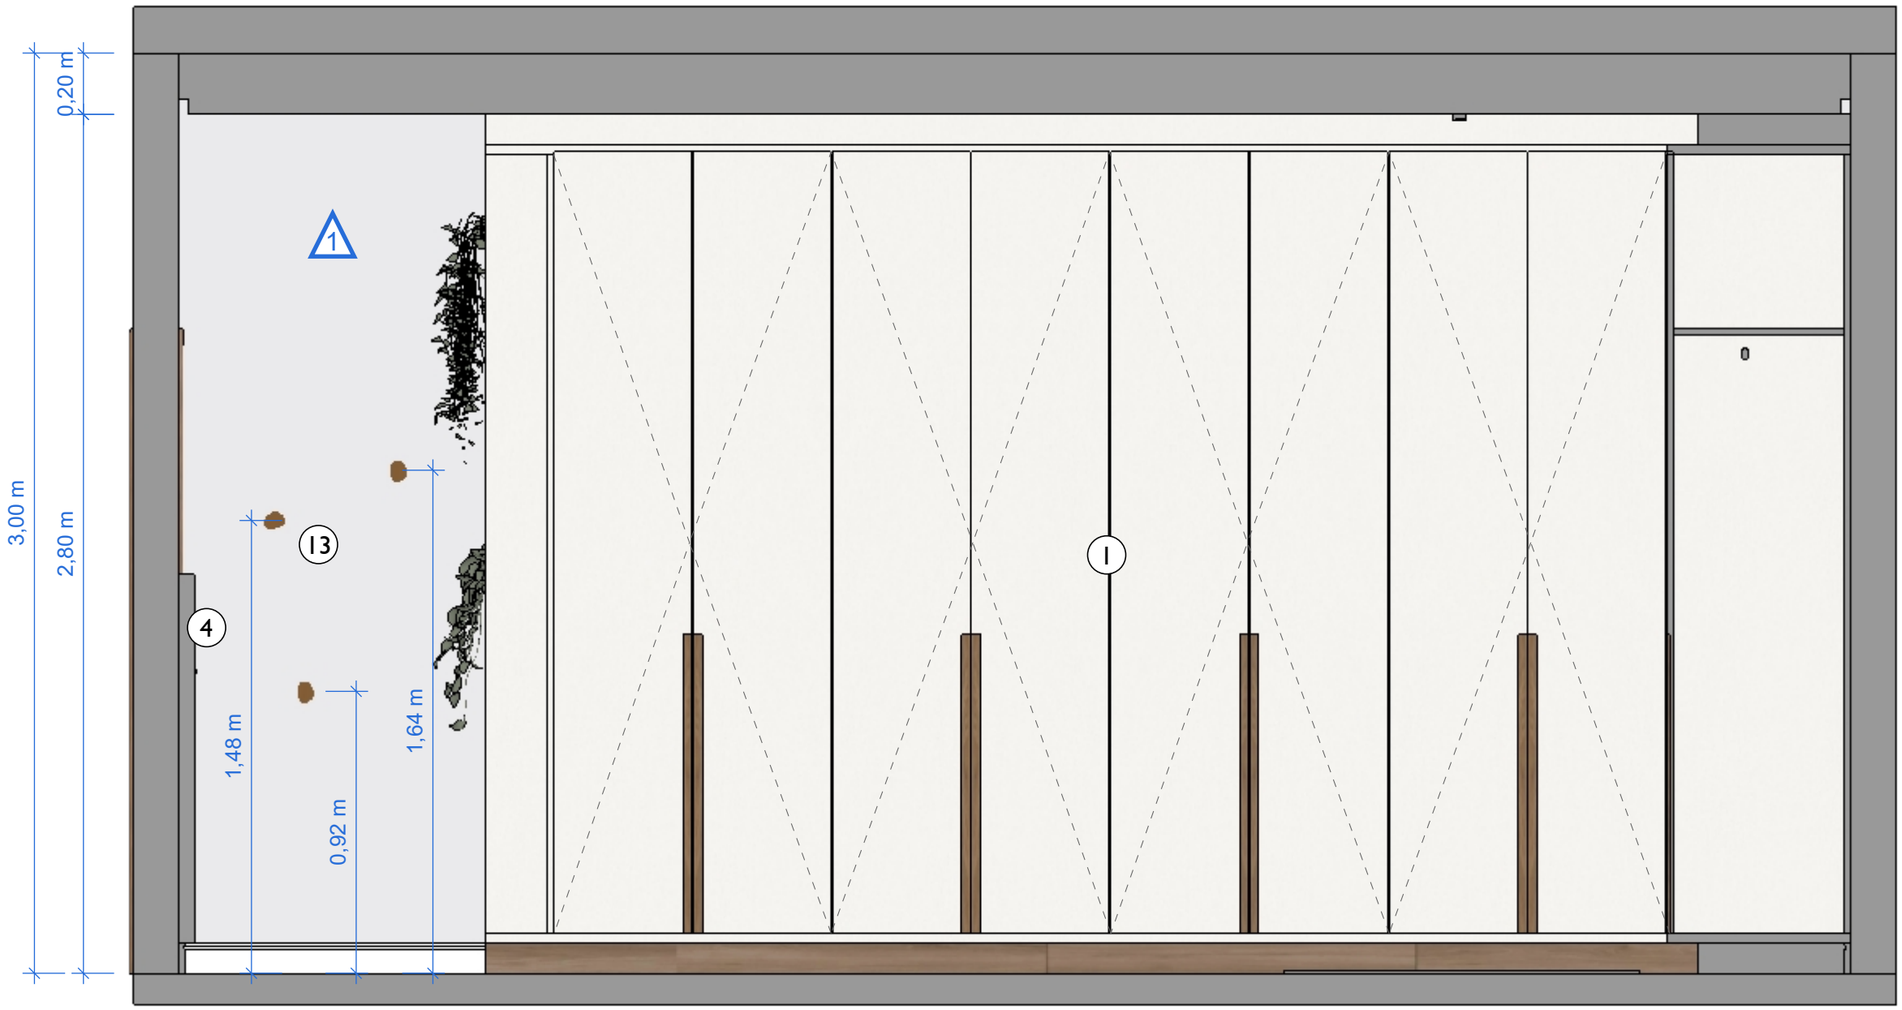

VISTA 04 - HUMANIZADA
escala: 1/20

QUARTO SUÍTE CAMILA E OTÁVIO
estúdio vilel[a]rq
Rua Jarbas Pimenta, nº 254 - Centro - Boa Esperança (MG)

João Paulo Vilela | tel.: (35) 99277-5071

estúdio vilel[a]rq
ARQUITETURA & DESIGN

ATENÇÃO: CONFERIR TODAS AS MEDIDAS NO LOCAL




VISTA 05 - HUMANIZADA
escala: 1/20

QUARTO SUÍTE CAMILA E OTÁVIO
estúdio vilel[a]rq
Rua Jarbas Pimenta, nº 254 - Centro - Boa Esperança (MG)


João Paulo Vilela | tel.: (35) 99277-5071

estúdio vilel[a]rq
ARQUITETURA & DESIGN


ATENÇÃO: CONFERIR TODAS AS MEDIDAS NO LOCAL

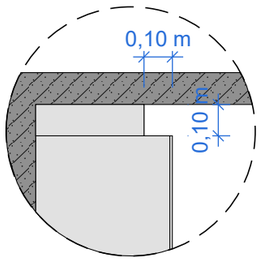

DET. RODATETO

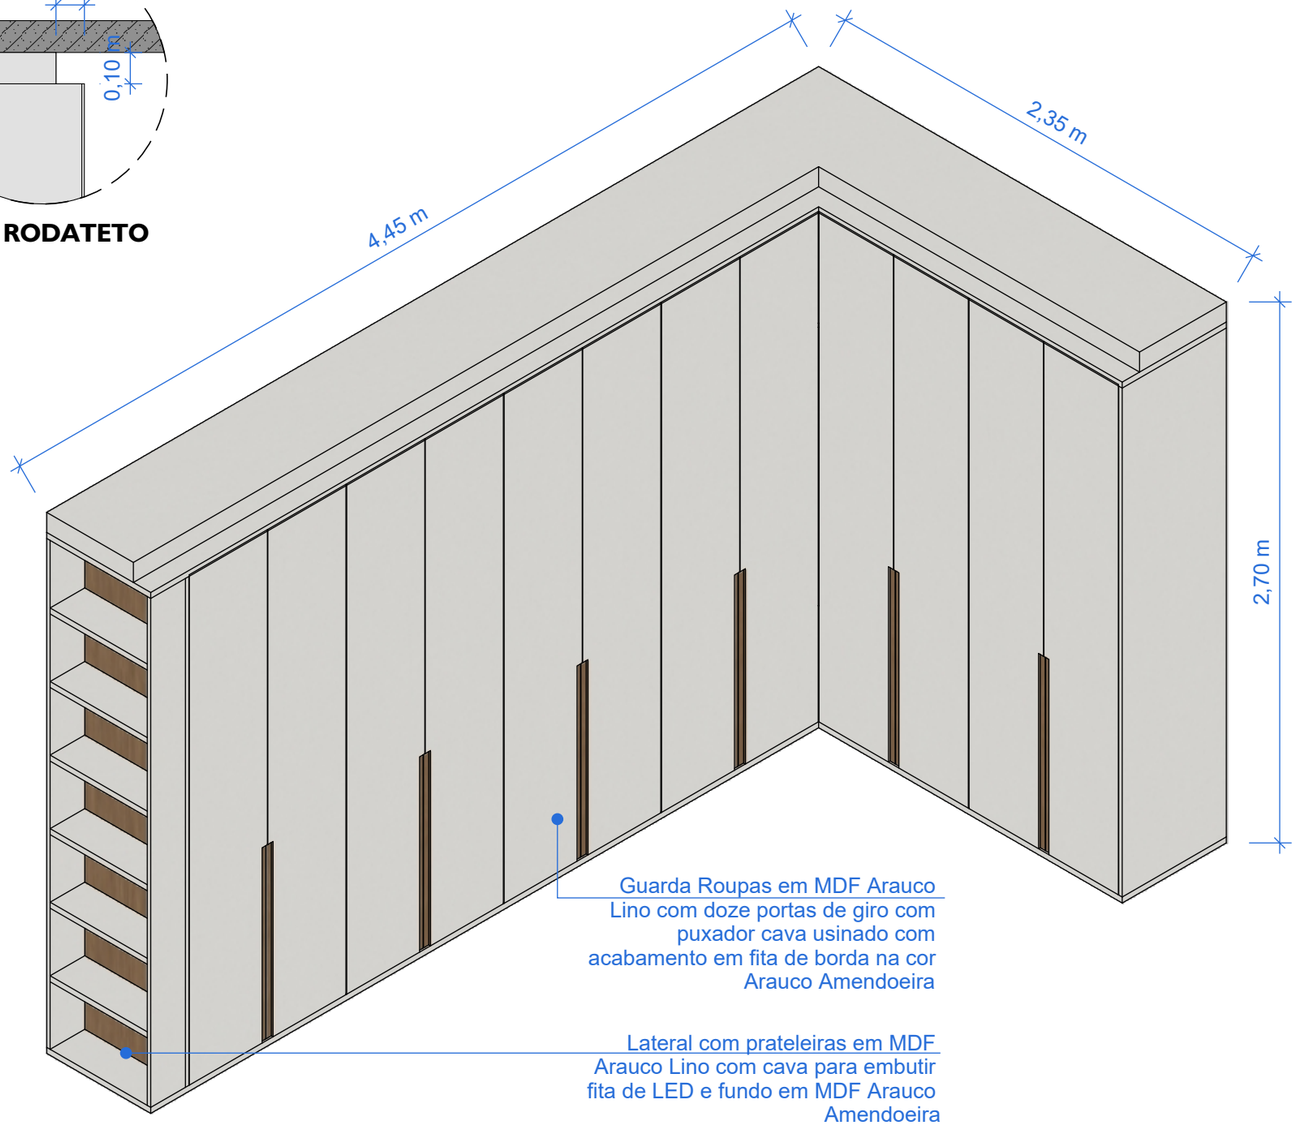

VISTA ISOMÉTRICA - MARCENARIA 01
escala: 1/25

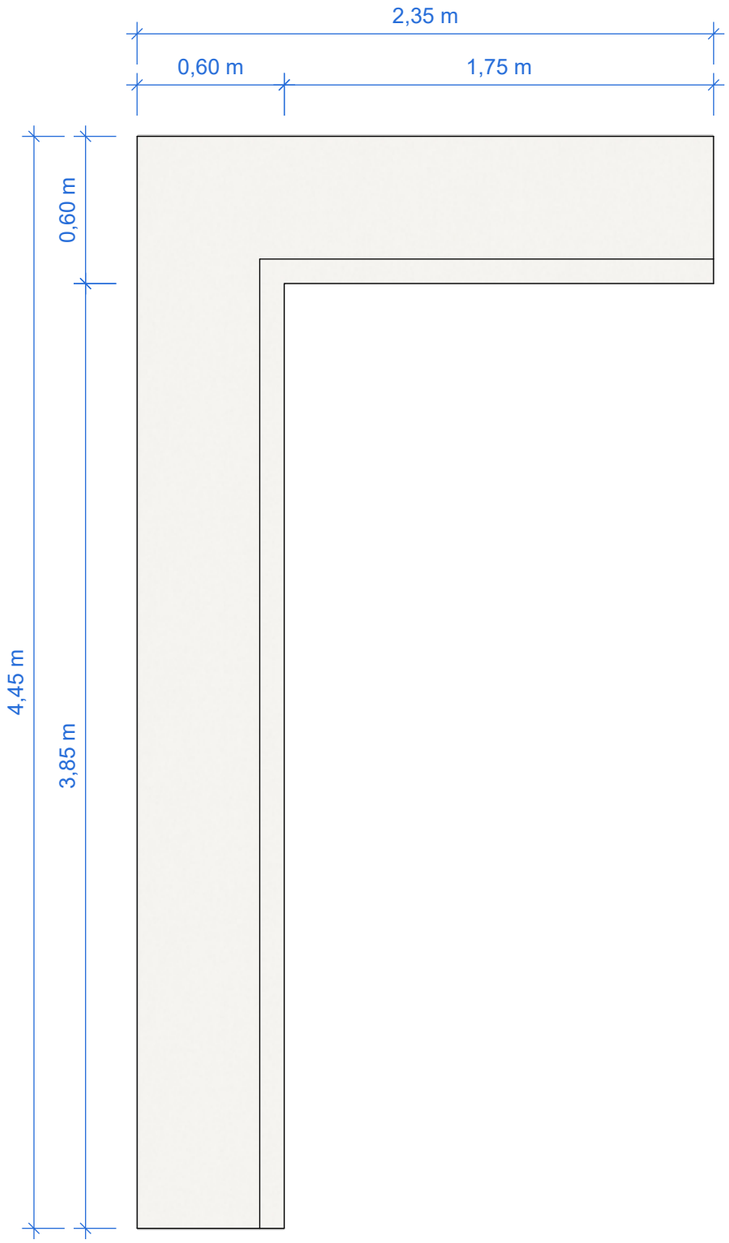


VISTA SUPERIOR - MARCENARIA 01
escala: 1/25

QUARTO SUÍTE CAMILA E OTÁVIO
estúdio vilel[a]rq
Rua Jarbas Pimenta, nº 254 - Centro - Boa Esperança (MG)


João Paulo Vilela | tel.: (35) 99277-5071

estúdio vilel[a]rq
ARQUITETURA & DESIGN

ATENÇÃO: CONFERIR TODAS AS MEDIDAS NO LOCAL

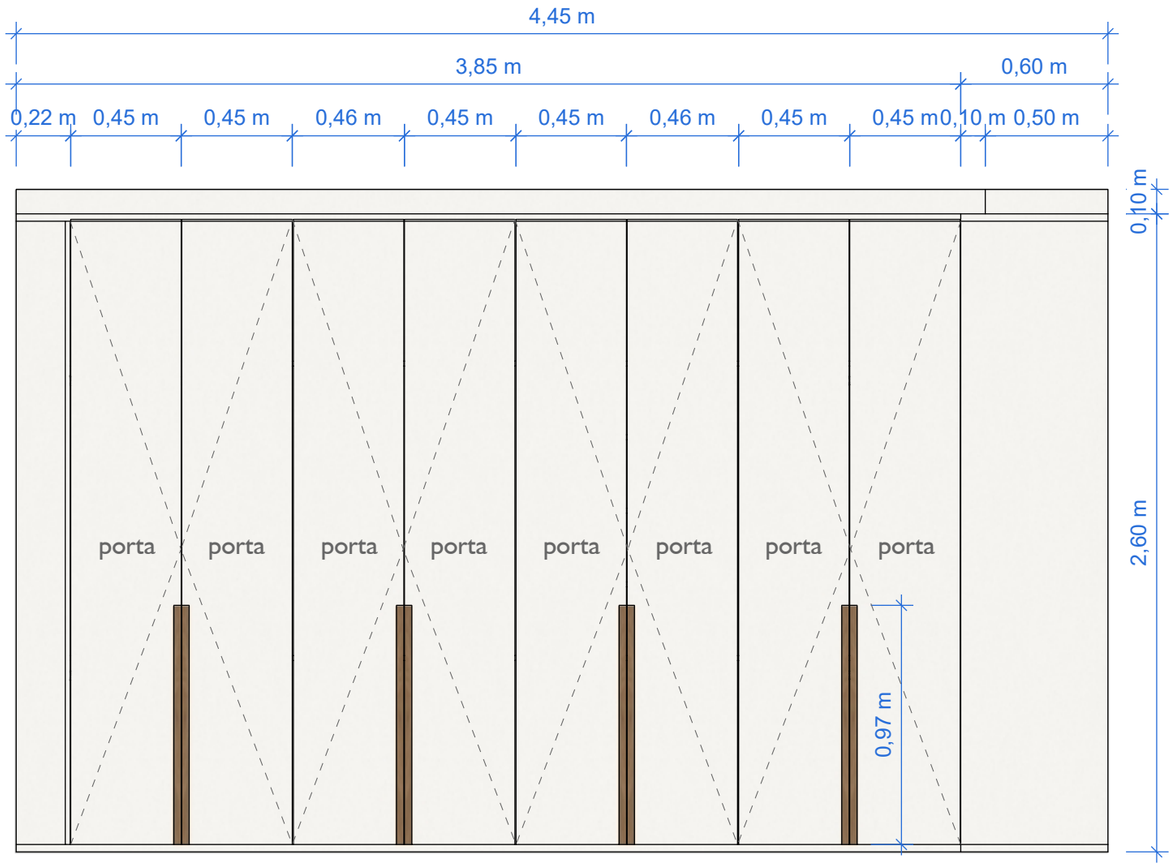

VISTA FRONTAL - MARCENARIA 01
escala: 1/25

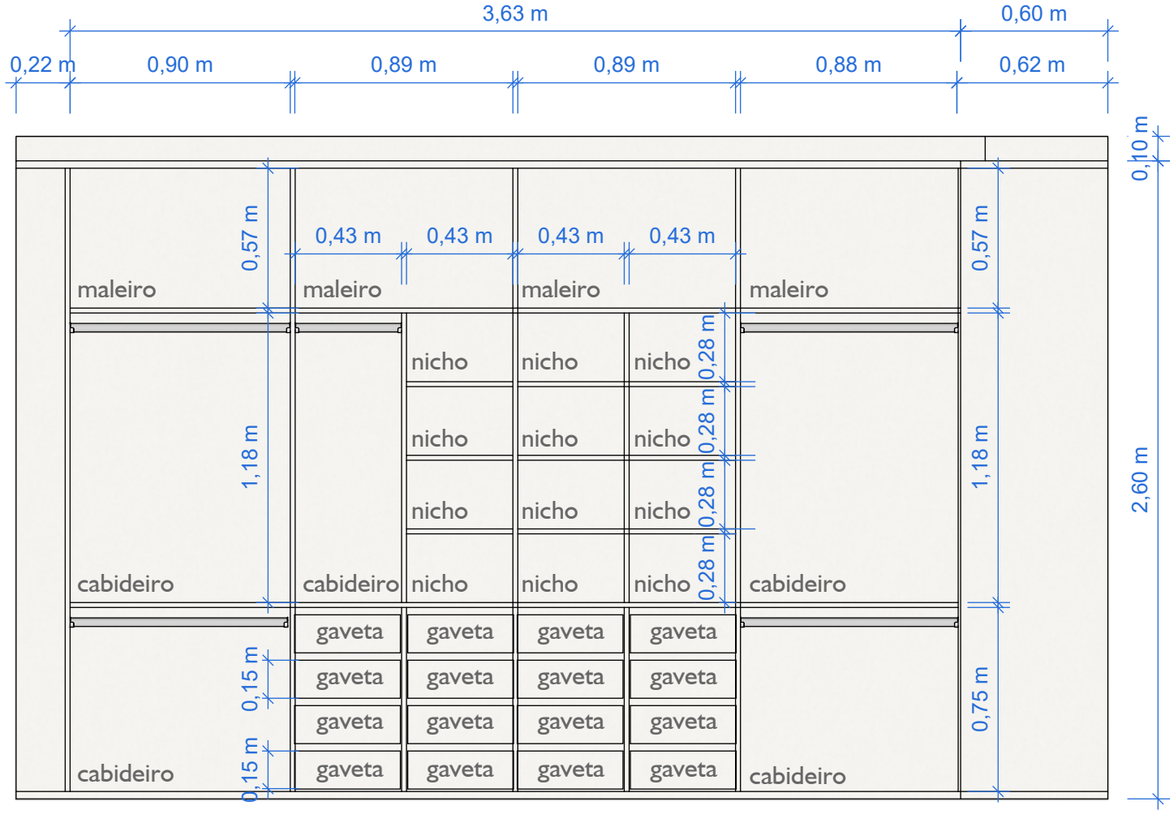


VISTA FRONTAL - MARCENARIA 01
escala: 1/25

QUARTO SUÍTE CAMILA E OTÁVIO
estúdio vilel[a]rq
Rua Jarbas Pimenta, nº 254 - Centro - Boa Esperança (MG)


João Paulo Vilela | tel.: (35) 99277-5071

estúdio vilel[a]rq
ARQUITETURA & DESIGN


ATENÇÃO: CONFERIR TODAS AS MEDIDAS NO LOCAL

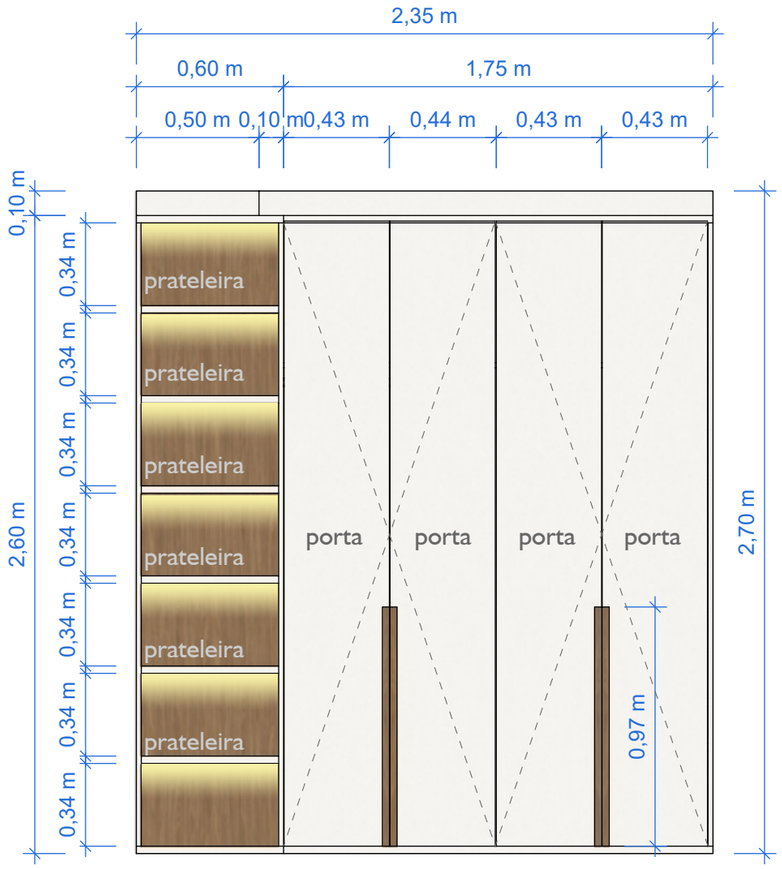

VISTA FRONTAL - MARCENARIA 01
escala: 1/25

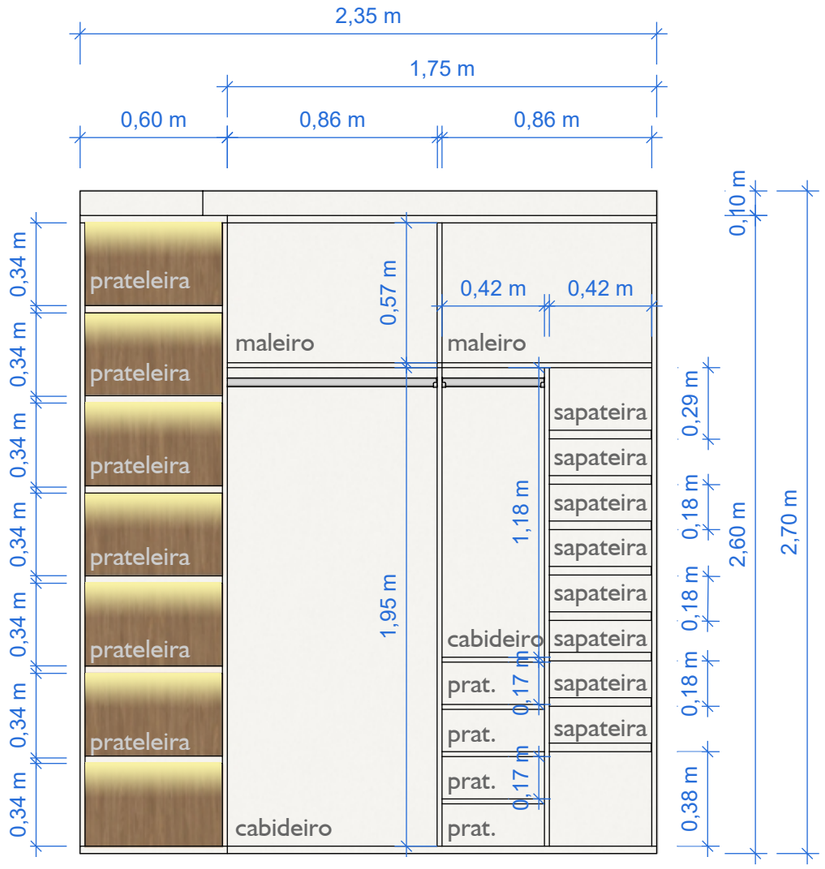

VISTA FRONTAL - MARCENARIA 01
escala: 1/25

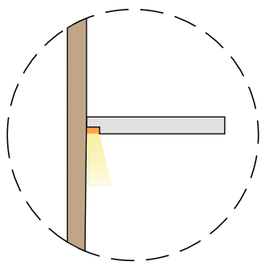


DET. CAVA FITA DE LED

QUARTO SUÍTE CAMILA E OTÁVIO
estúdio vilel[a]rq
Rua Jarbas Pimenta, nº 254 - Centro - Boa Esperança (MG)


João Paulo Vilela | tel.: (35) 99277-5071

estúdio vilel[a]rq
ARQUITETURA & DESIGN


ATENÇÃO: CONFERIR TODAS AS MEDIDAS NO LOCAL

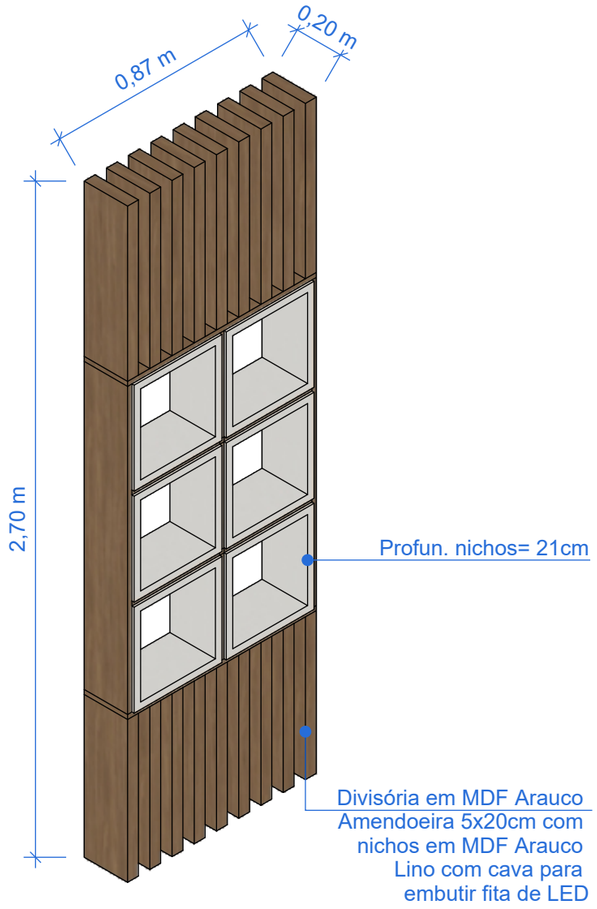


VISTA ISOMÉTRICA - MARCENARIA 02
escala: 1/20

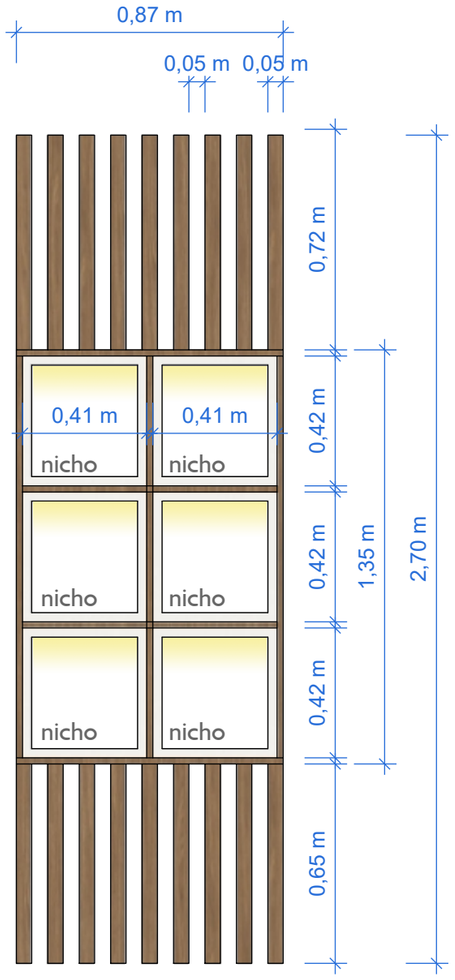


VISTA FRONTAL - MARCENARIA 02
escala: 1/20

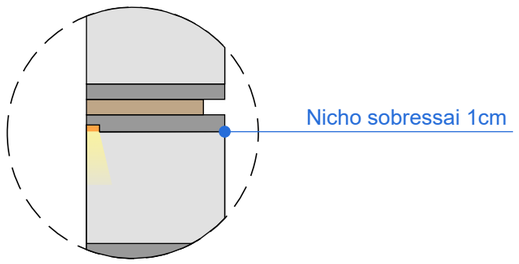

DET. CAVA FITA DE LED

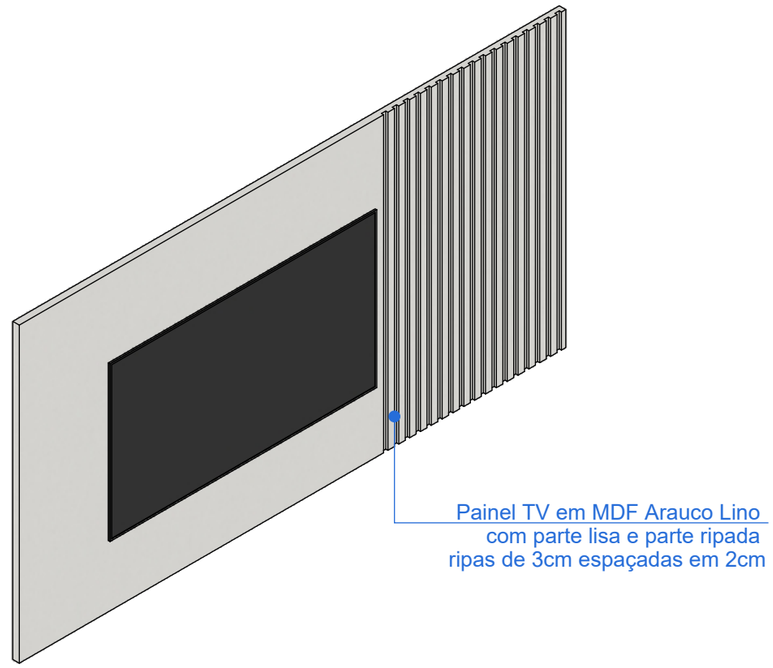

VISTA ISOMÉTRICA - MARCENARIA 03
escala: 1/20

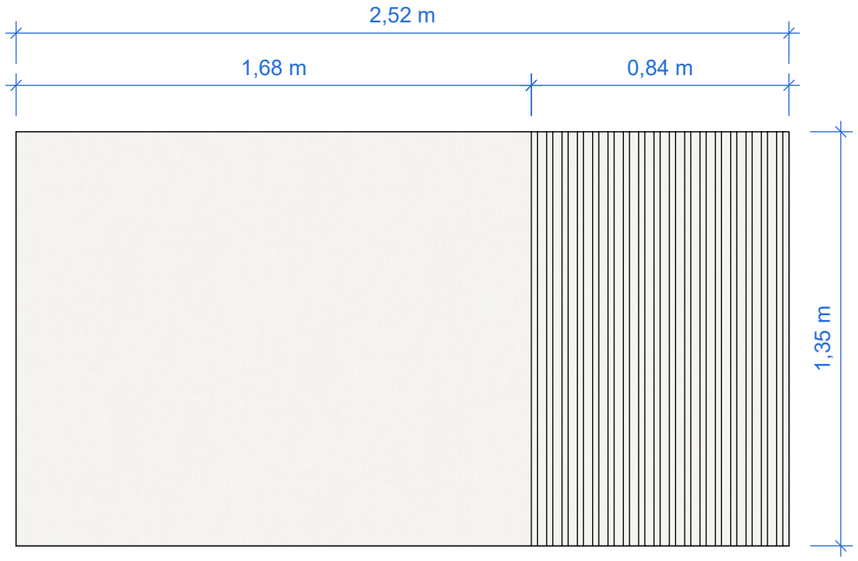


VISTA FRONTAL - MARCENARIA 03
escala: 1/20

QUARTO SUÍTE CAMILA E OTÁVIO
estúdio vilel[a]rq
Rua Jarbas Pimenta, nº 254 - Centro - Boa Esperança (MG)

João Paulo Vilela | tel.: (35) 99277-5071

estúdio vilel[a]rq
ARQUITETURA & DESIGN


ATENÇÃO: CONFERIR TODAS AS MEDIDAS NO LOCAL

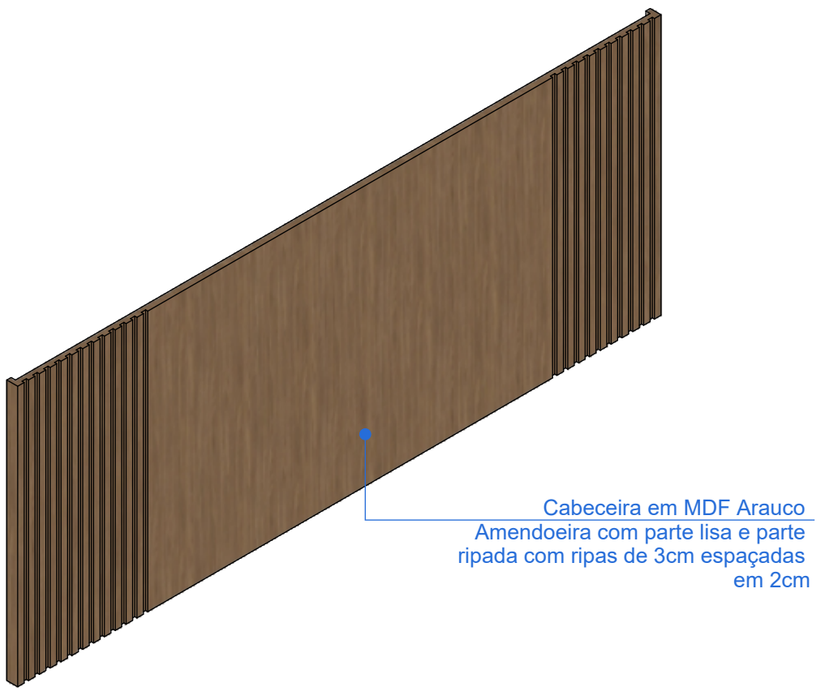


VISTA ISOMÉTRICA - MARCENARIA 04
escala: 1/20




VISTA FRONTAL - MARCENARIA 04
escala: 1/20

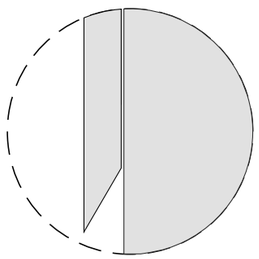


DET. PUXADOR CAVA INVERTIDO

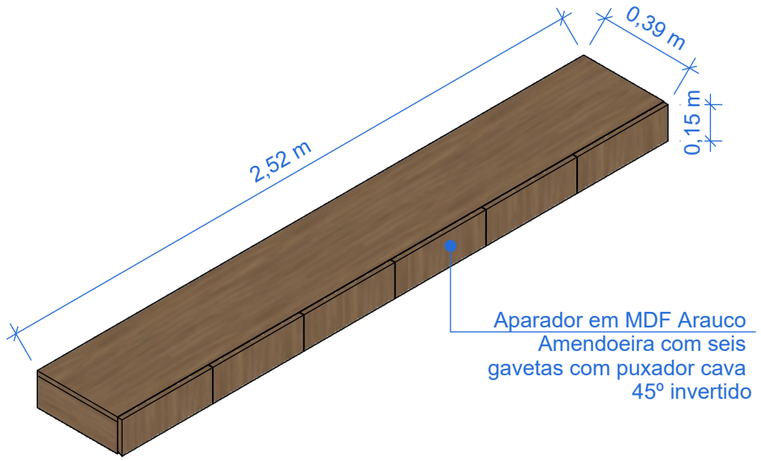


VISTA ISOMÉTRICA - MARCENARIA 05
escala: 1/20

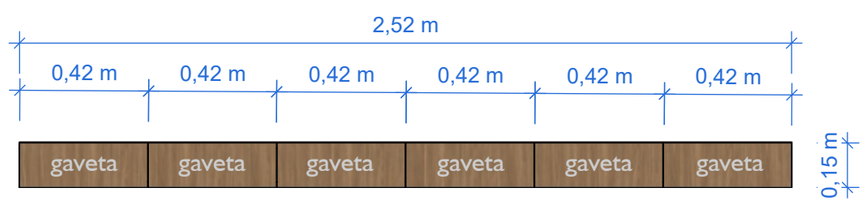

VISTA FRONTAL - MARCENARIA 05
escala: 1/20

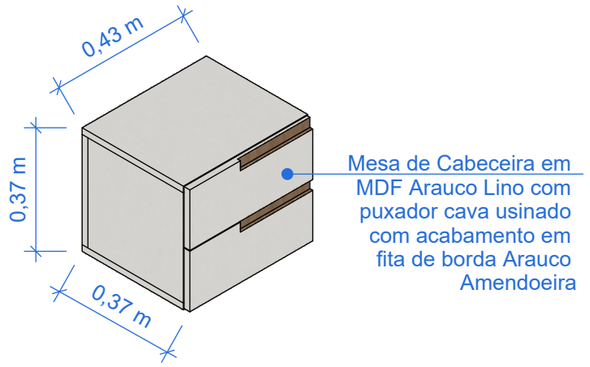

VISTA ISOMÉTRICA - MARCENARIA 06
escala: 1/15

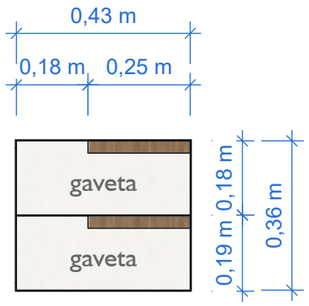


VISTA FRONTAL - MARCENARIA 06
escala: 1/15

QUARTO SUÍTE CAMILA E OTÁVIO
estúdio vilel[a]rq
Rua Jarbas Pimenta, nº 254 - Centro - Boa Esperança (MG)

João Paulo Vilela | tel.: (35) 99277-5071

estúdio vilel[a]rq
ARQUITETURA & DESIGN

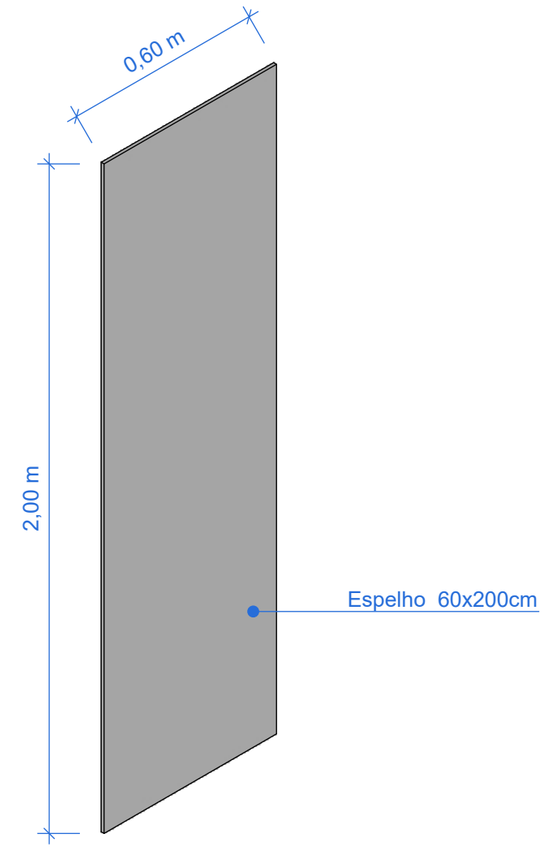

VISTA ISOMÉTRICA - VIDRAÇARIA 07
escala: 1/20

QUARTO SUÍTE CAMILA E OTÁVIO
estúdio vilel[a]rq
Rua Jarbas Pimenta, nº 254 - Centro - Boa Esperança (MG)

João Paulo Vilela | tel.: (35) 99277-5071